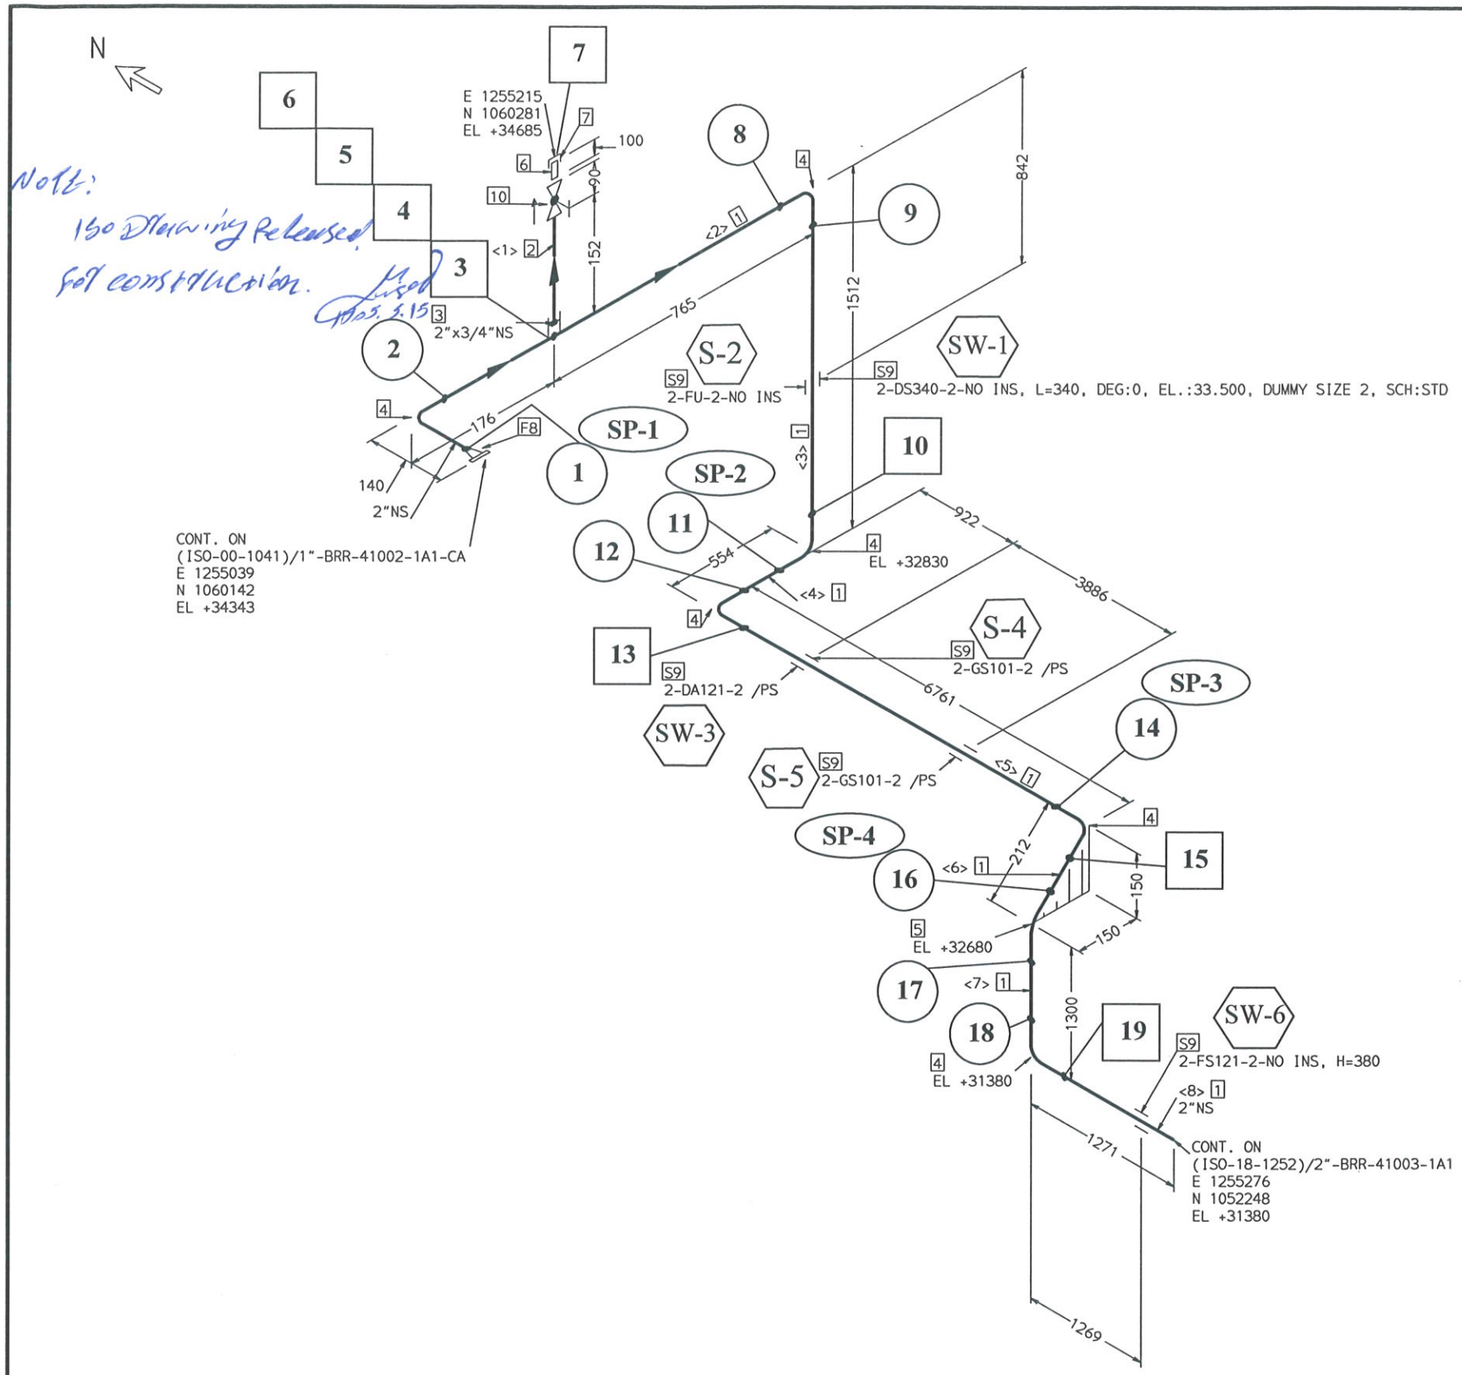


FABRICATION MATERIALS

PT NO	COMPONENT DESCRIPTION	N.S. (INS)	ITEM CODE	QTY
	PIPE			
1	PIPE S40 BE SMLS A333-6 ASME B36.10	2	P04A0G	11.7M
2	PIPE S80 PE SMLS A333-6 ASME B36.10	3/4	P08A0G	0.1M
	FITTINGS			
3	HALF COUPLING 3000# SW A350-LF2 CL.1 ASME B16.11	2 x 3/4	CH90SE0F	1
4	ELBOW 90 LR S40 BW A420-WPL6 ASME B16.9	2	EL04BE1C	6
5	ELBOW 45 LR S40 BW A420-WPL6 ASME B16.9	2	EK04BE1C	1
6	STRAIGHT NIPPLE S80 SMLS TOE A333-6 (L=100mm) ASME B36.10	3/4	NI08YNA0G	1
7	CAP 3000# NPT A350-LF2 CL.1 ASME B16.11	3/4	KA90NE0F	1
	FLANGES			
8	FLANGE WELDING NECK S40 150# RF A350-LF2 CL.1 ASME B16.5 SRF	2	F12W04RE0F	1
	SUPPORTS			
9	STRESS SUPPORT	2	1A1-ATTA-2"-	6

ERECTION MATERIALS

PT NO	COMPONENT DESCRIPTION	N.S. (INS)	ITEM CODE	QTY
	VALVES / IN-LINE ITEMS			
10	VALVE GLOBE 800# SW A350-LF2 CL.1 BODY W/304SS TRIM HF-BODY SEAT & DISC SEAT OSY-BB	3/4	VOU2S1	1

CUT PIPE LENGTH

PIECE NO	CUT LENGTH	N.S. (INS)	REMARKS	PIECE NO	CUT LENGTH	N.S. (INS)	REMARKS
<1>	100	3/4		<2>	789	2	
<3>	1360	2		<4>	402	2	
<5>	6609	2		<6>	101	2	
<7>	1189	2		<8>	1195	2	

PROJECT:	HDPE PLANT AND UTILITY (2146)
OWNER:	RAYAN POLYMER POUYA COMPANY
CONTRACTOR:	HAMPA ENERGY ENGINEERING & DESIGN COMPANY
DOCUMENT NO.:	2146-ISO-25-0010
LINE NO.:	2"-BRR-41003-1A1
ISOMETRIC NO:	ISO-25-1002
SHT NO:	1 /1
REF. P&ID DWG:	4101/8022
REF. PLAN DWG:	2146-10-20-DD-PI-DWG-0011-12

PRESSURE (barg.) DESIGN:	8,FV
PRESSURE (barg.) OPERATING:	2
TEMPERATURE (C.) DESIGN:	-15~85
TEMPERATURE (C.) OPERATING:	-5
INSULATION TYPE:	NO INS
INSULATION THK (mm):	0
TEST FLUID:	Water
TEST PRESSURE: (barg.)	12
PAINT:	P-1
NDT:	A
PWHT:	ASME B31.3
LOCATION:	AG
LEVEL:	2
LINE CLASS:	1A1

REV.	DATE	DESCRIPTION	PRE'D.	CHE'D BY	APP'D BY
0	01.08.2026	TOTALLY HOLD	M.IM	R.D	M.A

NOTE

1- ROOT GAPS OF BUTT WELD FITTINGS ARE NOT INCLUDED IN DIMENSIONS
2- ISOMETRIC DRAWING FOR 1 1/2" AND SMALLER PIPINGS ARE JUST FOR INFORMATION. PIPING ROUTING, DIMENSIONS AND ELEVATIONS TO BE CHECKED BY CONSTRUCTION CONSTRUCTOR BEFORE INSTALLATION.
3- FOR 1 1/2" AND SMALLER, SUPPORTS TO BE SELECTED BY CONSTRUCTION CONSTRUCTOR EXCEPT AS NOTED.
4- ACTUAL DIMENSION AND SIZE OF SPECIAL/INSTRUMENT ITEMS SHALL BE CHECKED BEFORE SPOOL FABRICATION BY CONSTRUCTION CONTRACTOR.

Piping Supervision
شرکت رایان پلیمر پویا
(سهامی خاص)
نظارت پایپینگ

Petro Parc Ghadir Co.

THIS DOCUMENT AND THE DESIGN IT COVERED IS THE PROPERTY OF POGO AND ALL RIGHTS ARE RESERVED. NEITHER IN WHOLE NOR IN PART MAY BE REPRODUCED OR TRANSMITTED TO THIRD PARTY WITHOUT PRIOR WRITTEN CONSENT OF OWNER.