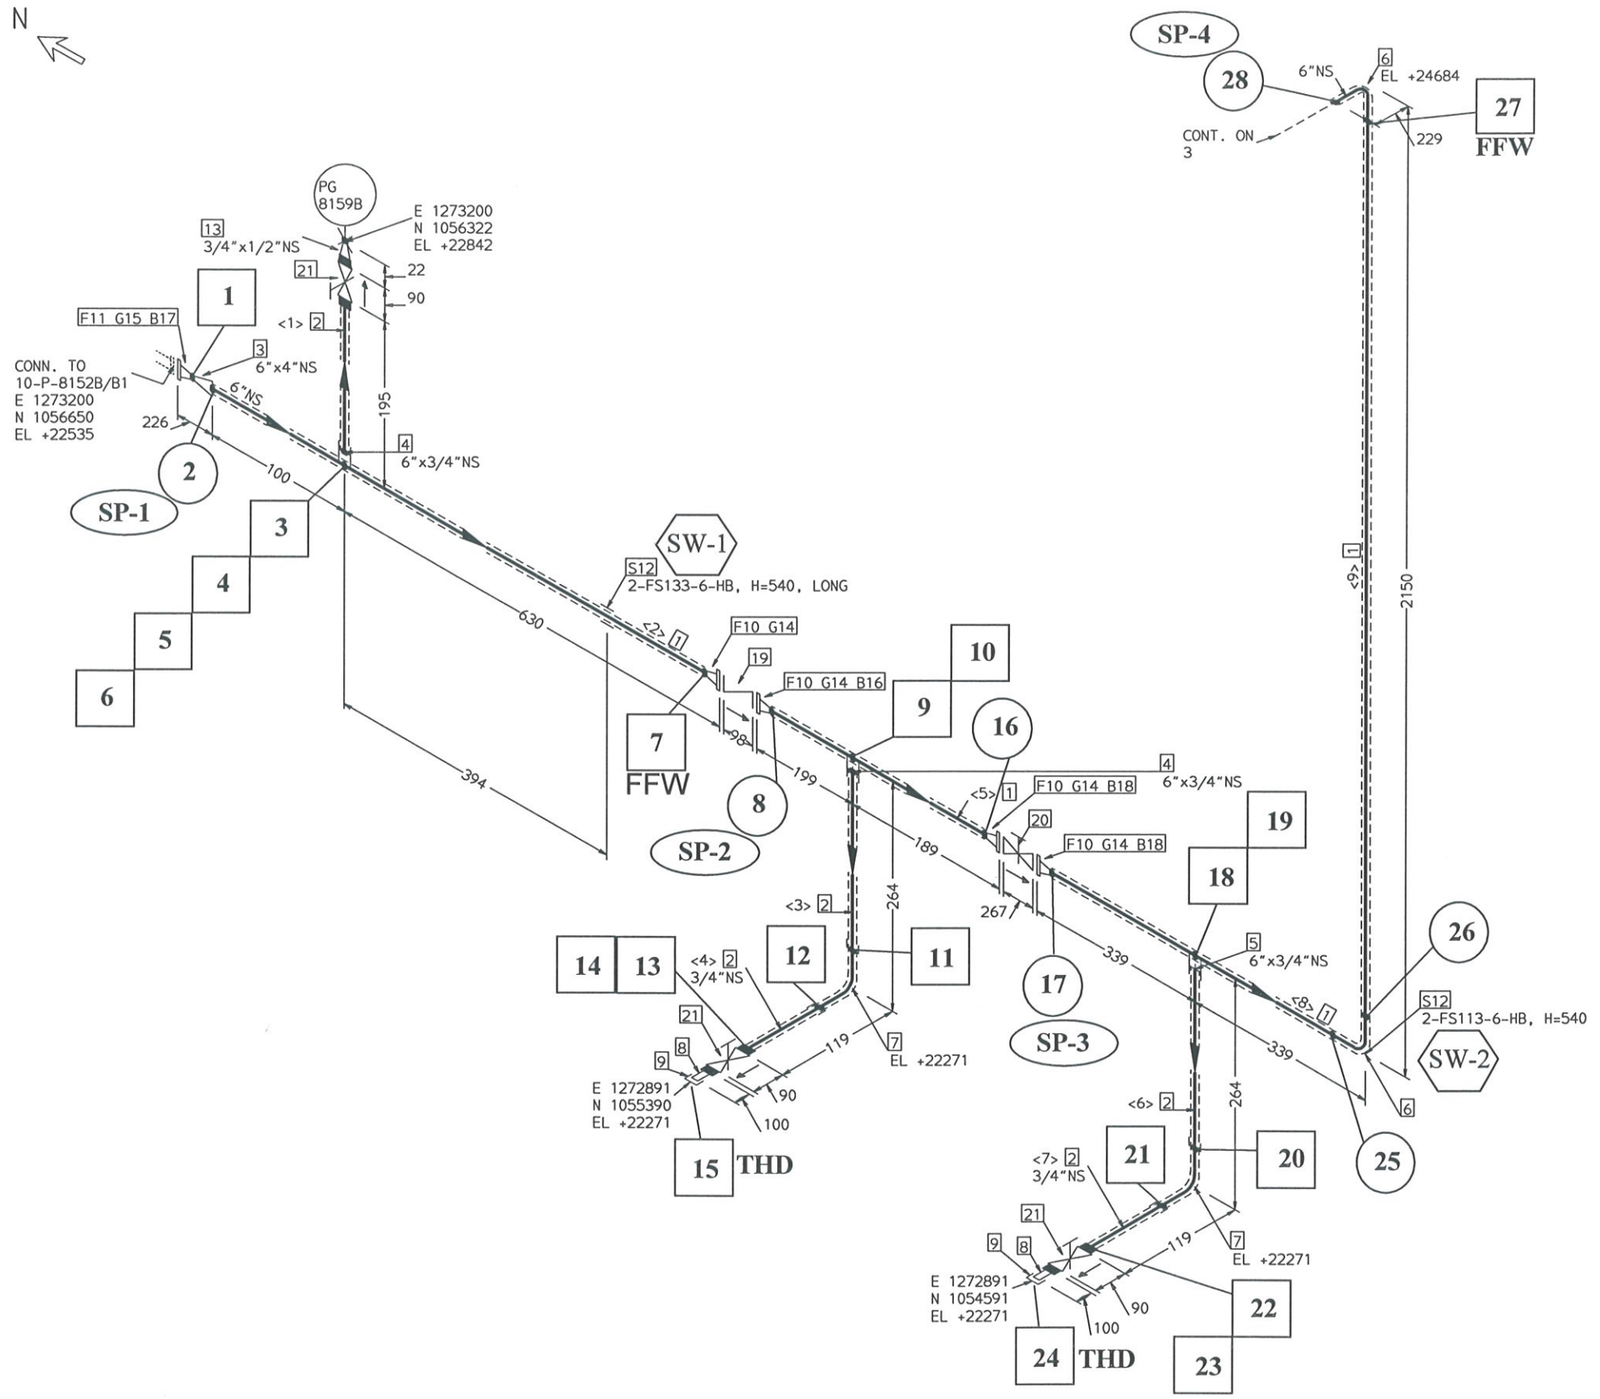



FABRICATION MATERIALS

| PT NO | COMPONENT DESCRIPTION | N.S. (INS) | ITEM CODE | QTY |
|---|---|---|---|---|
| | PIPE | | | |
| 1 | PIPE S40 BE ERW(EJ=0.85) API 5L-B PSL1 ASME B36.10 | 6 | P04D1A | 3.0M |
| 2 | PIPE S80 PE SMLS API 5L-B PSL1 ASME B36.10 | 3/4 | P08A0C | 0.6M |
| | FITTINGS | | | |
| 3 | REDUCER CONCENTRIC S40 S40 BW A234-WPBW ERW(EJ=0.85) ASME B16.9 | 6 x 4 | RC0404BE2A | 1 |
| 4 | HALF COUPLING 3000# SW A105 ASME B16.11 | 6 x 3/4 | CH90SE0A | 2 |
| 5 | HALF COUPLING 3000# NPT A105 ASME B16.11 | 6 x 3/4 | CH90NE0A | 1 |
| 6 | ELBOW 90 LR S40 BW A234-WPBW ERW(EJ=0.85) ASME B16.9 | 6 | EL04BE2A | 2 |
| 7 | ELBOW 90 3000# SW A105 ASME B16.11 | 3/4 | EL90SE0A | 2 |
| 8 | STRAIGHT NIPPLE S80 TOE SMLS API 5L-B PSL1 (L=100mm) ASME B36.10 | 3/4 | NI08YNA0C | 2 |
| 9 | CAP 3000# NPT A105 ASME B16.11 | 3/4 | KA90NE0A | 2 |
| | FLANGES | | | |
| 10 | FLANGE WELDING NECK S40 150# RF A105 ASME B16.5 SRF | 6 | F12W04RE0A | 4 |
| 11 | FLANGE WELDING NECK S40 300# RF A105 ASME B16.5 SRF | 4 | F14W04RE0A | 1 |
| | SUPPORTS | | | |
| 12 | STRESS SUPPORT | 6 | 1P2-ATTA-6"- | 2 |

ERECTION MATERIALS

| PT NO | COMPONENT DESCRIPTION | N.S. (INS) | ITEM CODE | QTY |
|---|---|---|---|---|
| | FITTINGS | | | |
| 13 | REDUCER INSERT 3000# PLE X TSE (NPTF) A105 MANUF. STD | 3/4 x 1/2 | RI90SE0A | 1 |
| | GASKETS | | | |
| 14 | GASKET 150# RF GRAPHITE W/SS REINFORCEMENT 2.0mm THK KLINGER PSM/AS or EQ. ASME B16.21 | 6 | G12S1Q20 | 4 |
| 15 | GASKET SPIRAL-WOUND 300# RF NON-ASBESTOS FILLER 304SS HOOP CS O.R. 4.5mm THK KLINGER MAXIFLEX CR or EQ. ASME B16.20 | 4 | G14V2R44 | 1 |
| | BOLTS | | | |
| 16 | 200 STUD BOLT ASTM A193 GR.B7 + 2 HEAVY HEX NUTS ASTM A194 GR.2H ASME B18.2 PTFE COATED | 3/4 | BSP0CUP | 8 |
| 17 | 120 STUD BOLT ASTM A193 GR.B7 + 2 HEAVY HEX NUTS ASTM A194 GR.2H ASME B18.2 PTFE COATED | 3/4 | BSP0CUP | 8 |
| 18 | 100 STUD BOLT ASTM A193 GR.B7 + 2 HEAVY HEX NUTS ASTM A194 GR.2H ASME B18.2 PTFE COATED | 3/4 | BSP0CUP | 16 |
| | VALVES / IN-LINE ITEMS | | | |
| 19 | VALVE CHECK 150# WAFER DUAL PLATE A216-WCB BODY W/13Cr DISC HF-BODY SEAT & DISC SEAT API 594 API 598 SRF | 6 | VCA1W4 | 1 |
| 20 | VALVE GATE 150# RF A216-WCB BODY W/13Cr TRIM HF-BODY SEAT & DISC SEAT OSY-BB FLEXIBLE WEDGE HAND WHEEL OP. | 6 | VGA1R3 | 1 |


* CONT. ON 2 *


| | |
|---|---|
| PROJECT: | HDPE PLANT AND UTILITY (2146) |
| OWNER: | RAYAN POLYMER POUYA COMPANY |
| CONTRACTOR: | HAMPA ENERGY ENGINEERING & DESIGN COMPANY |
| DOCUMENT NO.: | 2146-ISO-25-0010 |
| LINE NO.: | 6"-HWS-B1001-1P2-HB |
| ISOMETRIC NO.: | ISO-25-1020 |
| SHT NO.: | 1 /4 |
| REF. P&ID DWG.: | 8059 |
| REF. PLAN DWG.: | 2146-10-20-DD-PI-DWG-0011-12 |

| | |
|---|---|
| PRESSURE (barg.) DESIGN: | 8 , FV |
| PRESSURE (barg.) OPERATING: | 6.2 |
| TEMPERATURE (C.) DESIGN: | 120 |
| TEMPERATURE (C.) OPERATING: | 75-100 |
| INSULATION TYPE: | HB |
| INSULATION THK (mm): | 60 |
| TEST FLUID: | Water |
| TEST PRESSURE: (barg.) | 12.0 |

| | |
|---|---|
| PAINT: | P-4 |
| NDT: | A |
| PWHT: | ASME B31.3 |
| LOCATION: | AG |
| LEVEL: | 2 |
| LINE CLASS: | 1P2 |

| REV. | DATE | DESCRIPTION | PRE'D. | CHE'D BY | APP'D BY |
|---|---|---|---|---|---|
| 0 | 01.08.2026 | ISSUED FOR CONSTRUCTION | M.IM | R.D | M.A |

NOTE

1- ROOT GAPS OF BUTT WELD FITTINGS ARE NOT INCLUDED IN DIMENSIONS
2- ISOMETRIC DRAWING FOR 1 1/2" AND SMALLER PIPINGS ARE JUST FOR INFORMATION. PIPING ROUTING, DIMENSIONS AND ELEVATIONS TO BE CHECKED BY CONSTRUCTION CONSTRUCTOR BEFORE INSTALLATION.
3- FOR 1 1/2" AND SMALLER, SUPPORTS TO BE SELECTED BY CONSTRUCTION CONSTRUCTOR EXCEPT AS NOTED.
4- ACTUAL DIMENSION AND SIZE OF SPECIAL/INSTRUMENT ITEMS SHALL BE CHECKED BEFORE SPOOL FABRICATION BY CONSTRUCTION CONTRACTOR.

Piping Supervision
نظارت پایپینگ


THIS DOCUMENT AND THE DESIGN IT COVERS IS THE PROPERTY OF PDRO AND ALL RIGHTS ARE RESERVED. NEITHER IN WHOLE NOR IN PART MAY BE REPRODUCED OR TRANSMITTED TO THIRD PARTY WITHOUT PRIOR WRITTEN CONSENT OF OWNER.