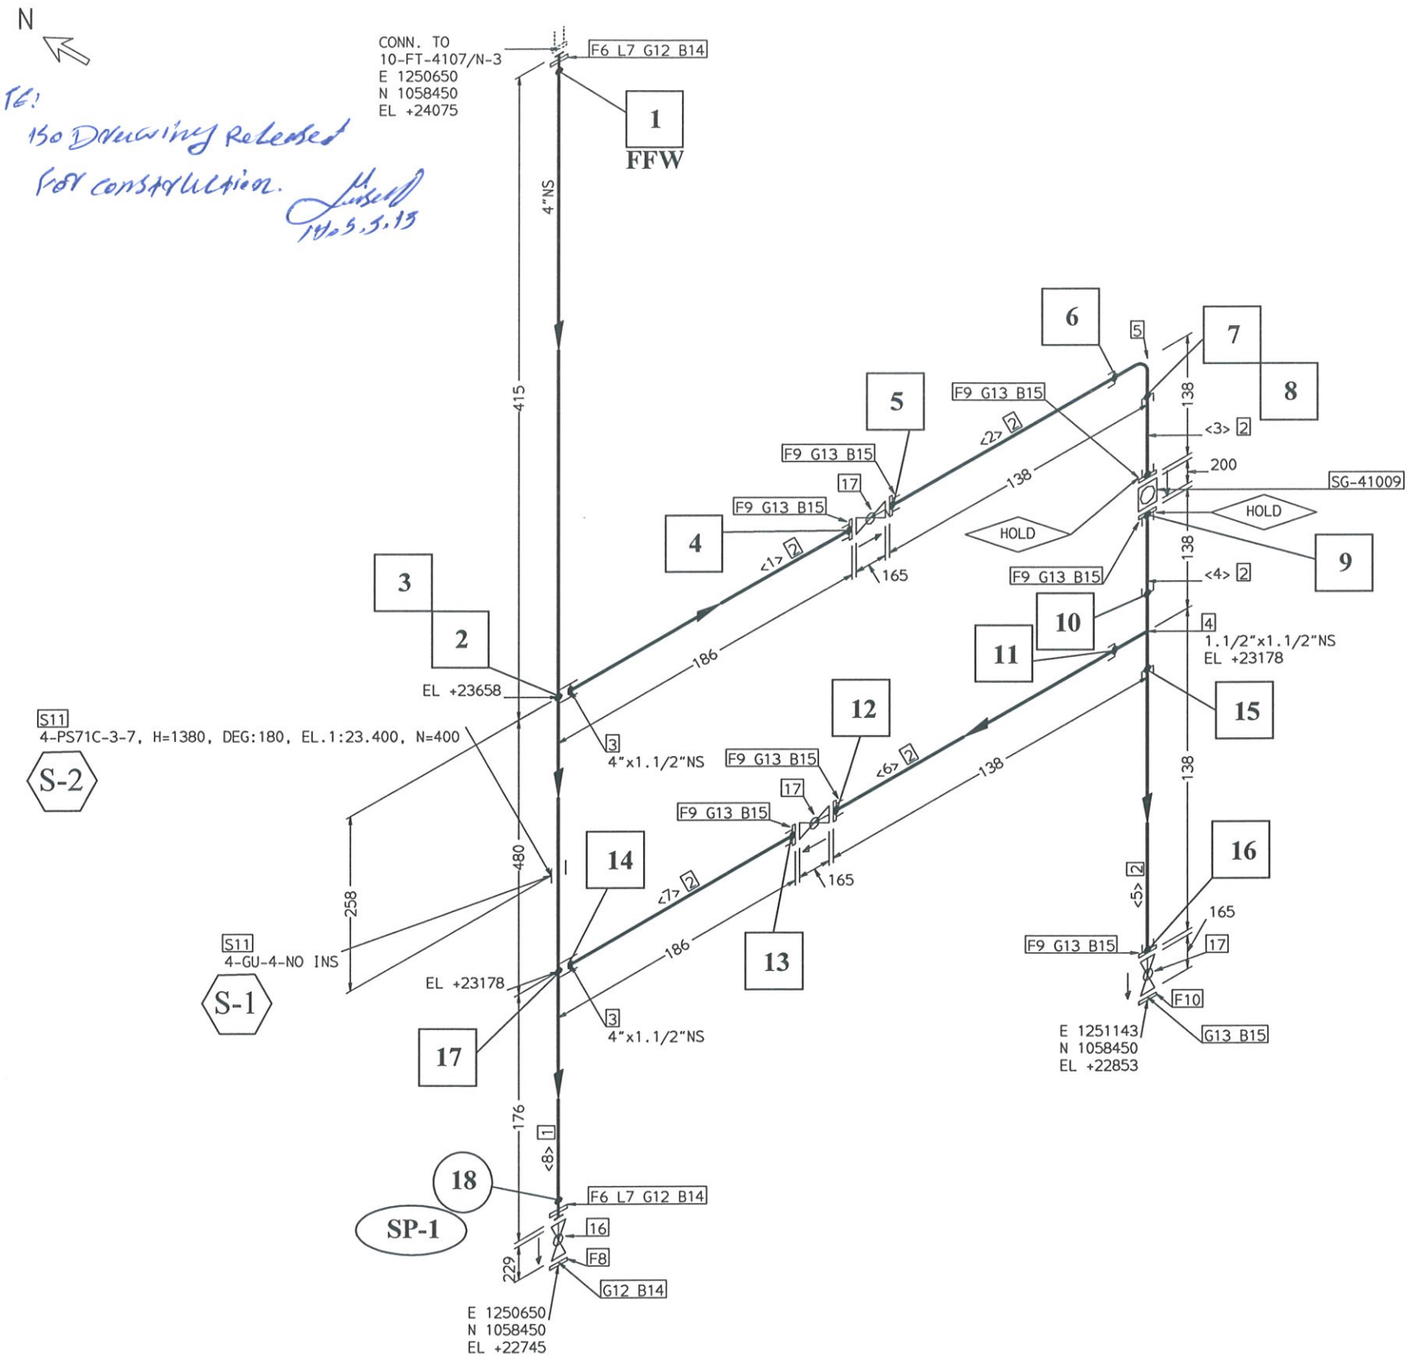


FABRICATION MATERIALS

PT NO	COMPONENT DESCRIPTION	N.S. (INS)	ITEM CODE	QTY
	PIPE			
1	PIPE 10S BE EFW(EJ=1) A312-TP304 ASME B36.19	4	P11C1A	1.0M
2	PIPE 40S PE SMLS A312-TP304 ASME B36.19	1.1/2	P74C0A	0.7M
	FITTINGS			
3	HALF COUPLING 3000# SW A182-F304 ASME B16.11	4 x 1.1/2	CH90SG0A	2
4	EQUAL TEE 3000# SW A182-F304 ASME B16.11	1.1/2 x 1.1/2	TT9090SG0A	1
5	ELBOW 90 3000# SW A182-F304 ASME B16.11	1.1/2	EL90SG0A	1
	FLANGES			
6	FLANGE LAP JOINT 150# FF A105 ASME B16.5	4	F12RAE0A	2
7	STUB END SP 10S BW A403-WP304-W EFW(EJ=1) ASME B16.9	4	S12E11RG2A	2
8	FLANGE BLIND 150# RF A182-F304 ASME B16.5 SRF	4	F12BRG0A	1
9	FLANGE SOCKET WELD 40S 150# RF A182-F304 ASME B16.5 SRF	1.1/2	F12K74RG0A	7
10	FLANGE BLIND 150# RF A182-F304 ASME B16.5 SRF	1.1/2	F12BRG0A	1
	SUPPORTS			
11	STRESS SUPPORT	4	1S1-ATTA-4"-	2

ERECTION MATERIALS

PT NO	COMPONENT DESCRIPTION	N.S. (INS)	ITEM CODE	QTY
	GASKETS			
12	GASKET 150# RF SHEET NON-ASBESTOS 2mm THK KLINGER C-4430 or EQ. ASME B16.21	4	G12S1Q19	3
13	GASKET 150# RF SHEET NON-ASBESTOS 2mm THK KLINGER C-4430 or EQ. ASME B16.21	1.1/2	G12S1Q19	8
	BOLTS			
14	90 STUD BOLT ASTM A193 GR.B7 + 2 HEAVY HEX NUTS ASTM A194 GR.2H ASME B18.2 PTFE COATED	5/8	BSP0CUP	24
15	70 STUD BOLT ASTM A193 GR.B7 + 2 HEAVY HEX NUTS ASTM A194 GR.2H ASME B18.2 PTFE COATED	1/2	BSP0CUP	32
	VALVES / IN-LINE ITEMS			
16	VALVE BALL 150# RF A351-CF8 BODY W/304SS BALL TEFLON SEAT FB FLOATING LEVER OP. LONG PA. ASME B16.10 API 608	4	VBA4R1	1
17	VALVE BALL 150# RF A351-CF8 BODY W/304SS BALL TEFLON SEAT FB FLOATING LEVER OP. LONG PA. ASME B16.10 API 608	1.1/2	VBA4R1	3

CUT PIPE LENGTH

PIECE NO	CUT LENGTH	N.S. (INS)	REMARKS	PIECE NO	CUT LENGTH	N.S. (INS)	REMARKS
<1>	100	1.1/2		<2>	100	1.1/2	
<3>	100	1.1/2		<4>	100	1.1/2	
<5>	100	1.1/2		<6>	100	1.1/2	
<7>	100	1.1/2		<8>	919	4	

PROJECT:	HDPE PLANT AND UTILITY (2146)
OWNER:	RAYAN POLYMER POUYA COMPANY
CONTRACTOR:	HAMPA ENERGY ENGINEERING & DESIGN COMPANY
DOCUMENT NO.:	2146-ISO-25-0010
LINE NO.:	4"-HX-41005-1S1
ISOMETRIC NO.:	ISO-25-1025
SHT NO.:	1 /1
REF. P&ID DWG.:	4101
REF. PLAN DWG.:	2146-10-20-DD-PI-DWG-0011-12

PRESSURE (barg) DESIGN:	-0.004&0.5
PRESSURE (barg) OPERATING:	0.1
TEMPERATURE (C.) DESIGN:	120
TEMPERATURE (C.) OPERATING:	100
INSULATION TYPE:	NO INS
INSULATION THK (mm):	0
TEST FLUID:	Air
TEST PRESSURE: (barg)	0.6
PAINT:	P-13
NDT:	B
PWHT:	ASME B31.3
LOCATION:	AG
LEVEL:	1
LINE CLASS:	1S1

REV.	DATE	DESCRIPTION	PRE'D.	CHE'D BY	APP'D BY
0	01.08.2026	TOTALLY HOLD	M.IM	R.D	M.A

NOTE
1- ROOT GAPS OF BUTT WELD FITTINGS ARE NOT INCLUDED IN DIMENSIONS
2- ISOMETRIC DRAWING FOR 1 1/2" AND SMALLER PIPINGS ARE JUST FOR INFORMATION. PIPING ROUTING, DIMENSIONS AND ELEVATIONS TO BE CHECKED BY CONSTRUCTION CONSTRUCTOR BEFORE INSTALLATION.
3- FOR 1 1/2" AND SMALLER, SUPPORTS TO BE SELECTED BY CONSTRUCTION CONSTRUCTOR EXCEPT AS NOTED.
4- ACTUAL DIMENSION AND SIZE OF SPECIAL/INSTRUMENT ITEMS SHALL BE CHECKED BEFORE SPOOL FABRICATION BY CONSTRUCTION CONTRACTOR.

Piping Supervision
نظارت پایپینگ

THIS DOCUMENT AND THE DESIGN IT COVERS IS THE PROPERTY OF POGC AND ALL RIGHTS ARE RESERVED. NEITHER IN WHOLE NOR IN PART MAY BE REPRODUCED OR TRANSMITTED TO THIRD PARTY WITHOUT PRIOR WRITTEN CONSENT OF OWNER.